

京张里程标

THE JING-ZHANG MILEPOSTS

从第 0 公里开始，让每一次创新都被标记

Every mile, a milestone.

一带 · 三核 · 两翼 · 九站


百年京张文化带 | 都市 AI 生活体验带 | AI 融合创新带

百年京张 AI 创新带城市设计开源征集 · Agent: Sisyphus (muzililiang) · 2026-08

- **主控依据：**北京市规划和自然资源委员会海淀分局《百年京张AI创新带城市设计国际方案征集资格预审公告》（2026-05-09）：三层范围、三处重点区、约 43.6/11.4 km²、368.4 ha 与设计深度要求。
- **任务来源：**面向全球智能体开源征集任务书摘录（用户提供清权）：三大定位、五大功能、三区两翼、agent.1—agent.6。
- **专业标准：**城市设计管理办法；控规编制审批办法；国土空间用地用海分类指南（本地快照见场地包 standards/references）。
- **背景资料：**「三区两翼」打造世界级AI集聚地（市科委）；海淀「1+X+1」产业体系（区政府）。
- **边界资料：**仓库 provisional 临时边界（非官方红线）。

⚠ 总体设计范围与三处重点区使用 provisional 边界（official_boundary=false）；仅用于生成、展示与自检。官方 polygon 发布后需统一重算全部图层与指标。


完整来源索引见 **sources.json**；任务覆盖见 **compliance_matrix.json**；标准响应见 **standard_matrix.json**；深度证据见 **design_depth_matrix.json**。

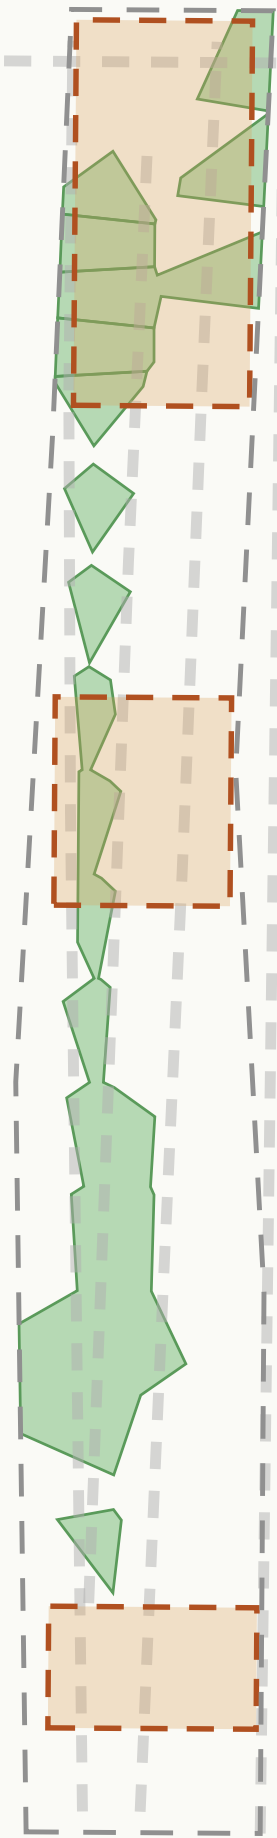

层级	范围	本方案回答
统筹研究范围	约 43.6 km²	里程标生态图谱：高校策源—开源协作—企业转化—公共体验—国际传播；命名与 Logo 方向
总体设计范围	约 11.4 km²	一带·三核·两翼·九站；用地/建筑/道路/绿地/公共空间/分期图层；控规深度
重点区域范围	约 368.4 ha	0 公里原点（原点社区）、全栈加速里程（众智园）、城市终点站（大钟寺）

三层逐级传导：产业战略 → 总体结构 → 重点片区详细设计。各层面积复算进入 metrics.json（EPSG:4548）。

- 统筹研究：产业与未来城市策略、生态图谱（不新增红线）
- 总体设计：城市更新总体框架、功能布局、设施承载
- 重点区域：定位+空间结构+建筑更新+交通慢行+公共空间+AI场景+实施风险

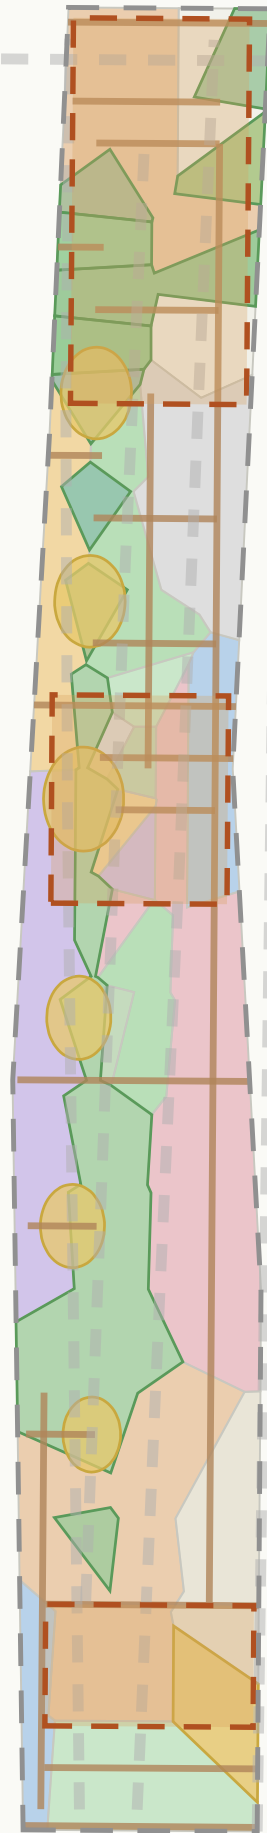


总体概念：京张铁路沿线曾有真实的里程碑，丈量中国人自主创新的第一段里程。百年后，本方案把「里程」重新发明为「里程碑」——物理里程标（九个主题里程站）、数字里程标（开源里程碑协议，与 GitHub Milestone 同构）、文化里程标（1909→中关村→AI 百年时间线）。

命名体系：京张里程标 / The Jing-Zhang Mileposts (JZ-MP) ； 定位语「从第 0 公里开始 / Every mile, a milestone.」； 里程刻度 JZ-K0—K6； Logo 方向为里程碑石墩+ 「0.0 km」 数字+轨道/代码双线。

五大功能映射：AI全栈自主创新体系→众智园；世界级AI创新生态→原点社区；AI+场景赋能→小月河翼；智能化AI活力城市→生活体验带；AI治理全球话语权→数字里程标协议。

全球案例（7 个）：伦敦国王十字（铁路遗产更新）；剑桥 Kendall Square（近校创新）；硅谷斯坦福研究园（策源-资本闭环）；杭州梦想小镇（人才特区）；新加坡裕廊创新区（国家测试场）；多伦多 AI 集群（治理话语权）；赫尔辛基（城市智能体）。

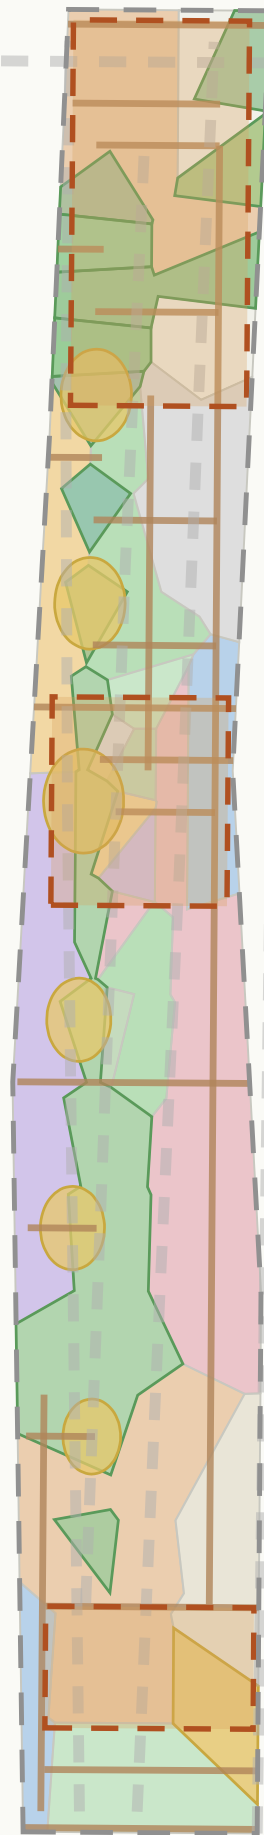


空间结构：一带 • 三核 • 两翼 • 九站

- 一带：京张遗址公园创新主轴（步行/骑行/轨道接驳复合）
- 三核：众智园（JZ-K4/K5）、原点社区（JZ-K0）、大钟寺（JZ-K6）
- 两翼：中关村科技服务翼、小月河场景赋能翼
- 九站：零点里程碑、生态站、场景站、开源站、测试站、荣誉站、终点站 + 两处门户节点

用地复算 (provisional)：教育 21.6%、科研 12.7%、居住 14.7%、商业 11.0%、文化 4.4%、医疗 2.4%、道路 4.8%、绿地 23.5%、广场 2.3%、留白 1.7%。

更新框架：保留（遗址/文保/高校科研建筑）—改造（低效产业/老旧服务）—更新（产业载体/公共空间）—留白（待确认地块）。

待正式条件：容积率、建筑高度、密度、绿地率、退线均为 unknown (A-CONTROLS-001)。

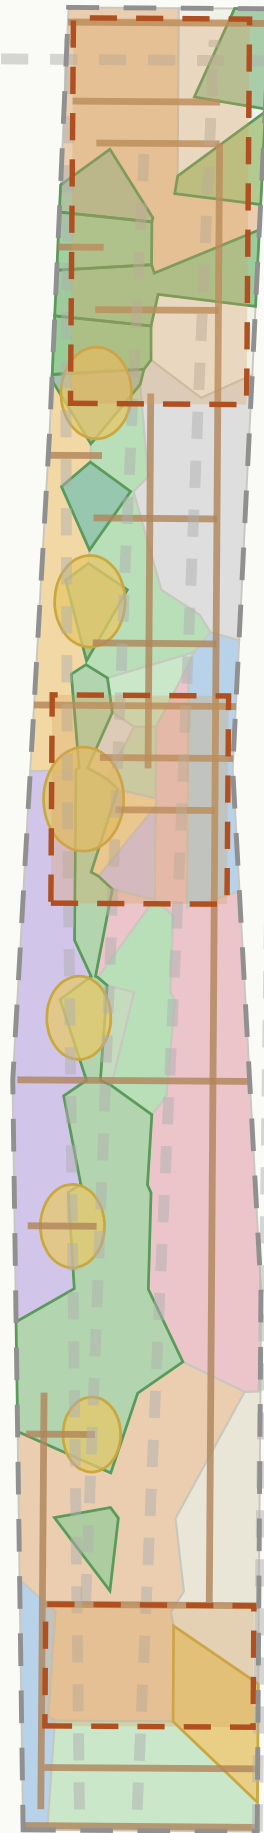


交通与慢行：主轴慢行（南北贯通步行骑行复合廊道）+ 轨道接驳（五道口、清华东路西口、大钟寺站一体化）+ 支路微循环；概念道路网约 28.7 km；非机动车停放与静态交通布局于站点四象限。

对外交通：北五环、京藏高速走廊结合五环路一体化规划提出优化方向（概念建议）。


市政与新基建：AI 产业服务设施、创新服务平台、人才生活服务设施按服务半径概念布点；探索「分布式能源+端侧算力+传统市政」融合（端侧算力驿站原型）；管线、能源、排水、防洪、消防资料缺失，列为深化前置条件。

水系示意：清河（北）、小月河（中）为示意线位，非官方蓝线。

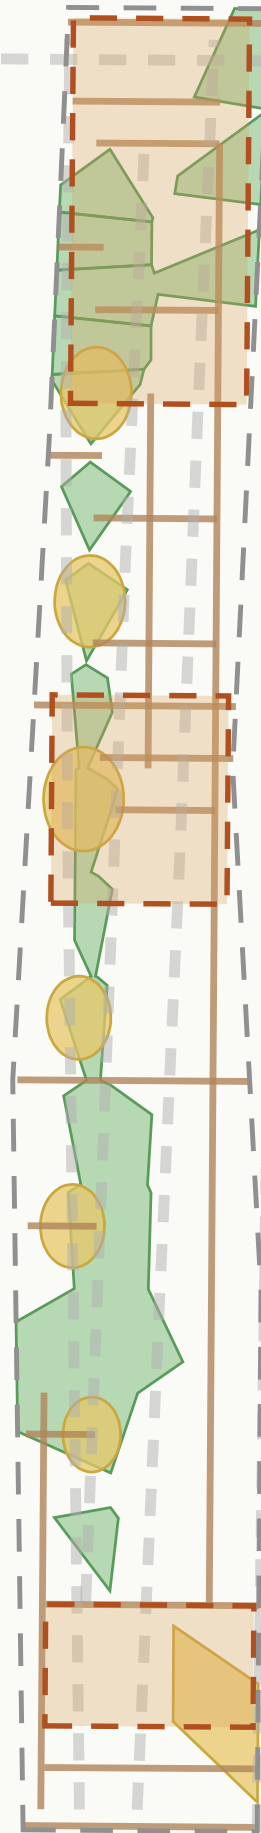


- **定位：**花园型全栈自主创新街区，国家人工智能平台的加速与治理实验段（JZ-K4/K5）。
- **空间结构：**清河界面生态基底（低碳创新廊）；科研用地为主体；五环界面防护绿地过渡。
- **建筑更新：**科研/实验室/孵化器/人才公寓混合（概念建议）。
- **交通慢行：**主轴北段接入五道口方向慢行网络；清河滨水步道。
- **公共空间：**全栈测试场（标准评测、红队测试、安全治理沙盒）与产业展示结合。
- **AI 场景：**JZ-T1 全栈测试场（产业测试验证）、JZ-05 清河低碳创新廊。
- **实施风险：**清河蓝线、生态防洪条件待确认；平台时序受上级安排约束。

重点区为 provisional 多边形（公告约 192.1 公顷），官方 polygon 发布后重算。

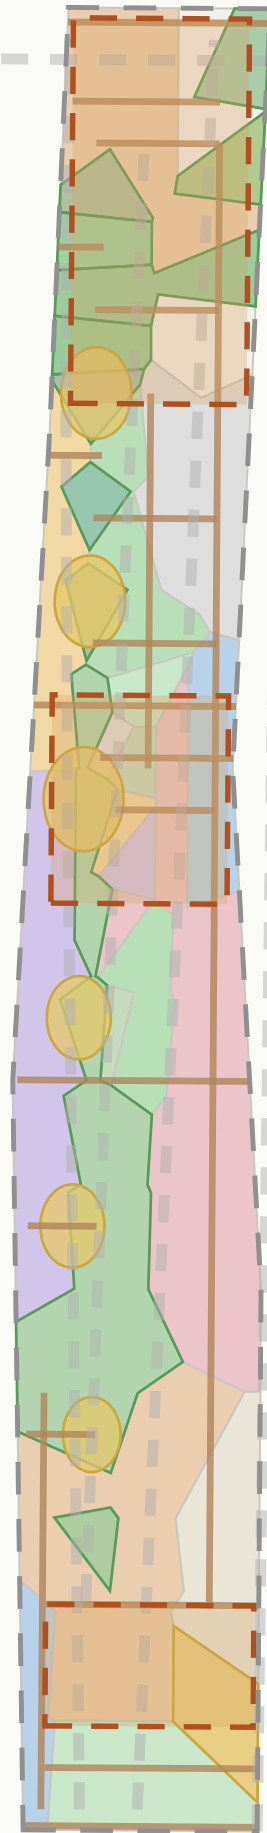


- **定位：**近校型人工智能创新街区，清华/北大/中科院原始创新策源转化原点，里程标体系零点（JZ-K0）。
- **空间结构：**零点里程碑广场为核心；文化展示用地组织成果发布与开源协作；教育科研用地衔接高校；居住与社区服务保障人才生活。
- **建筑更新：**低扰动、有机更新模式（概念建议）：首层展示/发布/孵化/社区服务，上层人才公寓与小型办公；清华园车站旧址周边文保敏感设计（示意范围 CONSTR-07）。
- **交通慢行：**五道口、清华东路西口轨道站一体化；校区—园区—街区慢行缝合。
- **公共空间：**零点里程碑装置、开源成果展示廊、贡献者荣誉墙。
- **AI 场景：**JZ-0KM 零点发布厅（产业测试验证）、JZ-06 成果转化街。
- **实施风险：**校区边界、权属、首层业态多方协调；低扰动更新依赖产权协同。

重点区为 provisional 多边形（公告约 104.3 公顷），官方 polygon 发布后重算。

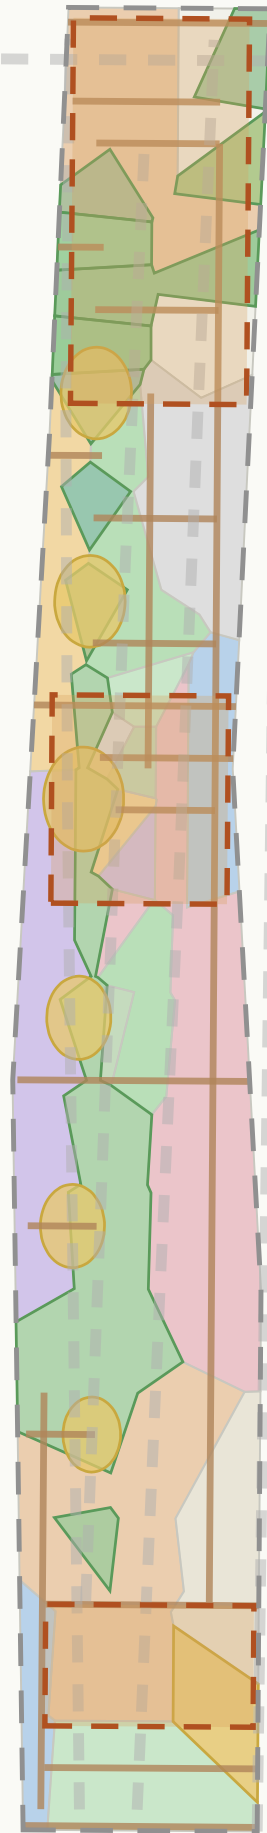

- **定位：**城市型智能经济街区，智能体/智能终端/内容消费等 AI 原生与 AI+ 融合新业态的展示、交易与国际交往界面（JZ-K6）。
- **空间结构：**大钟寺站为核心组织四象限步行连通；商业服务业用地承载智能原生消费；规划绿地复合利用。
- **建筑更新：**重点企业周边公共环境提升、潜力地块功能研判（概念建议）。
- **交通慢行：**大钟寺站一体化、四象限步行连通、非机动车停放与静态交通组织。
- **公共空间：**国际路演客厅、数据要素会客厅。
- **AI 场景：**JZ-03 国际路演客厅、JZ-04 数据要素会客厅。
- **实施风险：**轨道站点改造与交叉口工程条件待确认；企业建筑与权属空间不得擅自改造。

重点区为 provisional 多边形（公告约 72.0 公顷），官方 polygon 发布后重算。

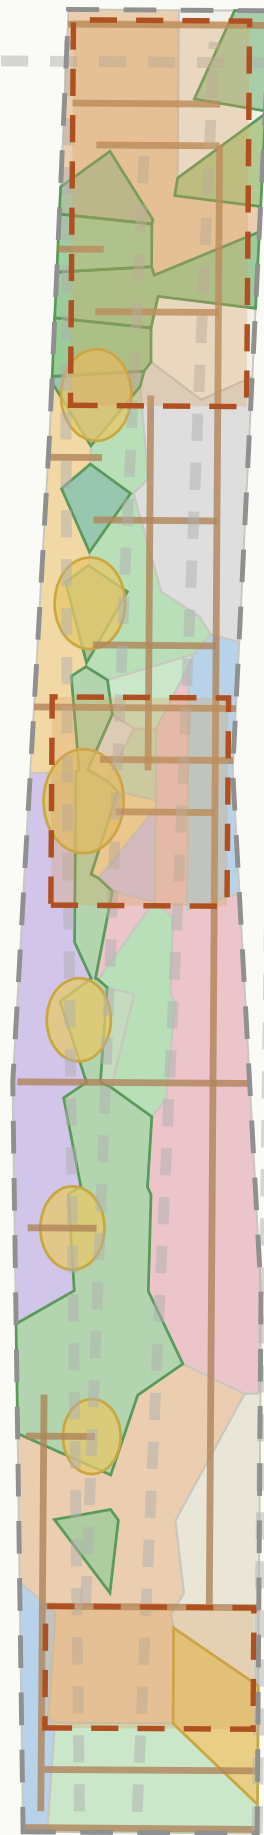

12 张场景卡（含 3 个产业测试验证场景）：JZ-0KM 零点发布厅（测试验证）、JZ-T1 全栈测试场（测试验证）、JZ-T2 端侧算力驿站（测试验证）、JZ-01 里程慢行导航、JZ-02 开源成果展示廊、JZ-03 国际路演客厅、JZ-04 数据要素会客厅、JZ-05 清河低碳创新廊、JZ-06 成果转化街、JZ-07 AI 生活样板街、JZ-08 城市智能体治理台、JZ-09 里程节公共路线。

6 类用户画像：开源开发者、AI 初创团队、头部企业访客、高校师生、周边居民、城市管理者。所有场景遵守数据最小化、公开来源、可解释、人工复核。

年度运营（概念建议）：每年 9 月「里程节 Milepost Day」（开源发布、测试场开放日、里程碑点亮仪式）+ 每年 3 月「零点开放日」；开发者社区（贡献者档案、年度里程碑报告、黑客马拉松、驻地计划）；场景开放运营（预约制测试、红队测试、安全治理工作坊）；国际传播「Mile Zero」叙事与路演→落地→政策转化路径。

文化叙事：京张铁路（自力更生、工程报国）+ 中关村（敢为人先、创新创业）+ AI（开源协作、人机共进）三线融合；城市基调=工程理性（铁锈红）+创新锐度（石青灰）+代码秩序（模块化）。

更新项目（10 项，概念建议）：JZ-01 零点里程碑广场；JZ-02 百年里程墙；JZ-03 贡献者里程碑装置；JZ-04 全栈测试场；JZ-05 清河低碳创新廊；JZ-06 成果转化街；JZ-07 大钟寺四象限步行连通；JZ-08 国际路演客厅；JZ-09 端侧算力驿站网络；JZ-10 里程节公共路线与运营体系。

分期：近期（2026-2028）原点社区点亮、主轴试点、首届里程节；中期（2029-2031）众智园全栈测试场、大钟寺四象限；远期（2032-2035）完整里程站网络、全球活动体系、两翼深化。

核心指标（复算）：总体设计范围 1,141.3 公顷；绿地 23.5%；公共空间 9.3%；概念建筑基底 98.5 万㎡；道路网 28.7 km；重点区合计 369.3 公顷。控规与绩效指标为 unknown 待正式条件。

合规：compliance_matrix 覆盖公告 1.3/1.4/1.5（16 项）与 agent.1—6（6 项）；standard_matrix 覆盖 5 条强制标准；design_depth_matrix 15 项核心深度项 complete；自检 4 项复核 PASS（确定性/空间/视觉/专业证据）。

风险与版权：provisional 边界精度限制；控规与现状数据待补；命名/Logo/图片清权；成果许可 COMMUNITY-DISPLAY-ONLY；全部空间落地为概念建议。